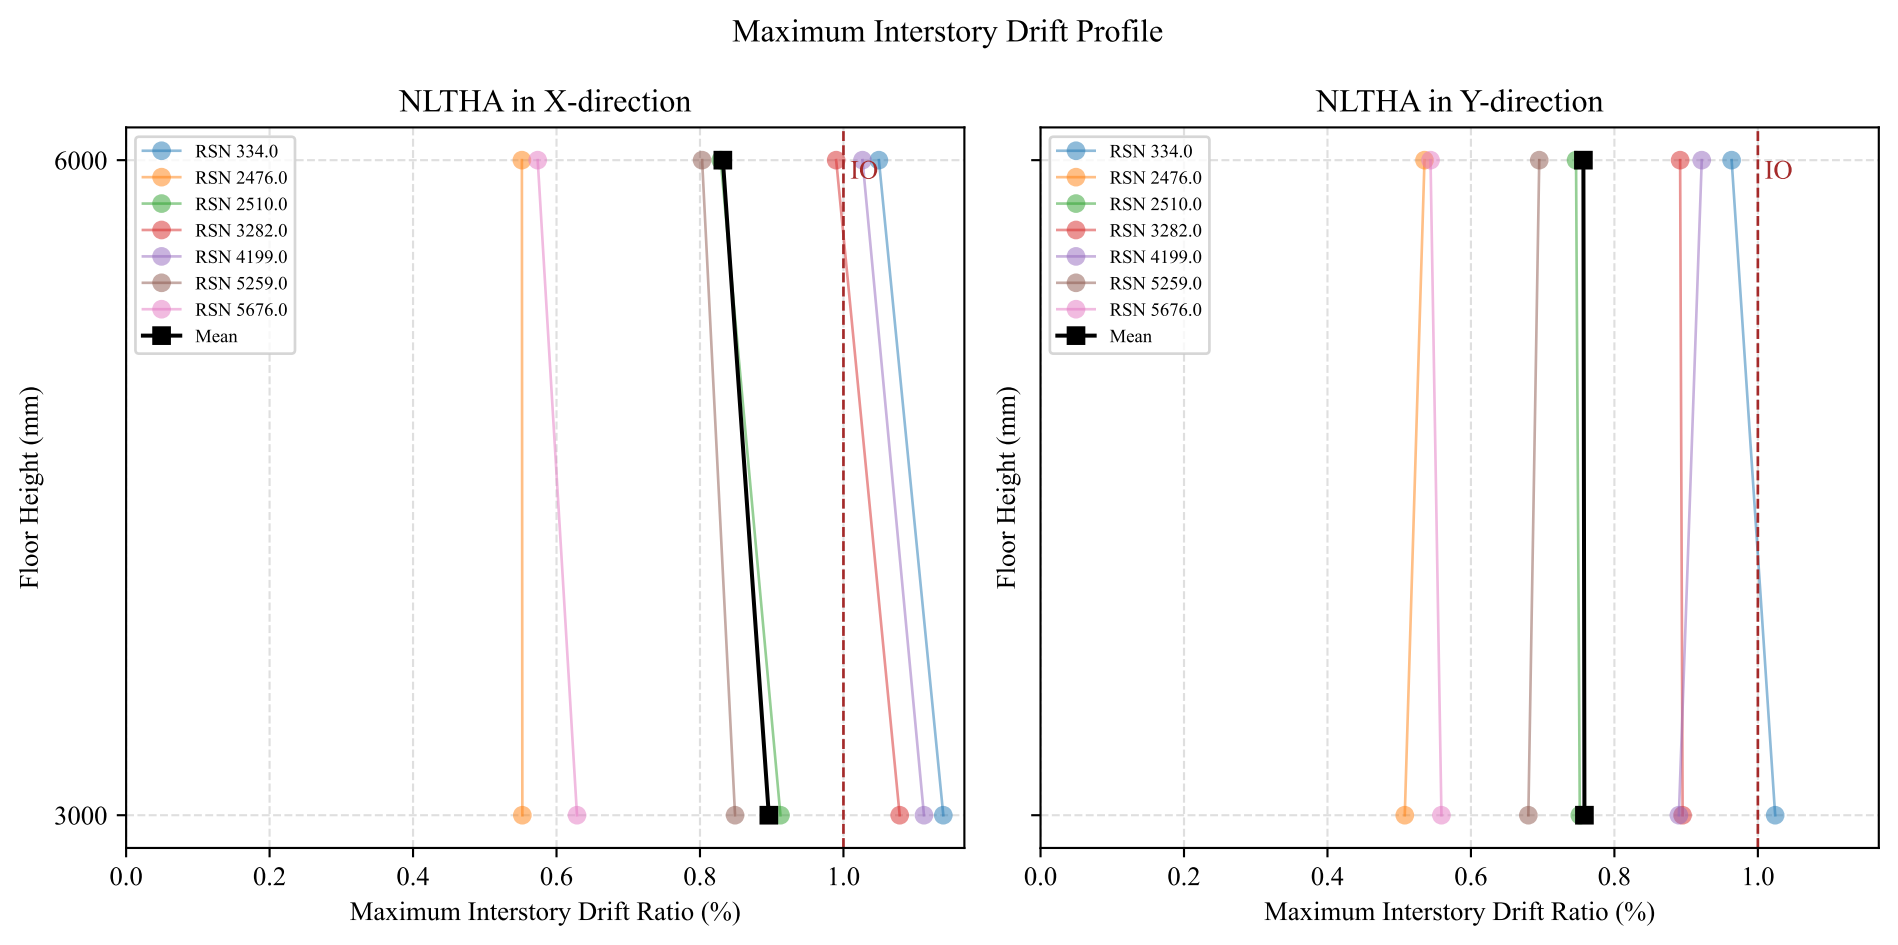
Maximum Interstory Drift Profile
NLTHA in X-direction
NLTHA in Y-direction
RSN 334.0
RSN 2476.0
RSN 2510.0
RSN 3282.0
RSN 4199.0
RSN 5259.0
RSN 5676.0
Mean
IO
6000
3000
Floor Height (mm)
0.0
0.2
0.4
0.6
0.8
1.0
Maximum Interstory Drift Ratio (%)